


Экспликация зданий и сооружений

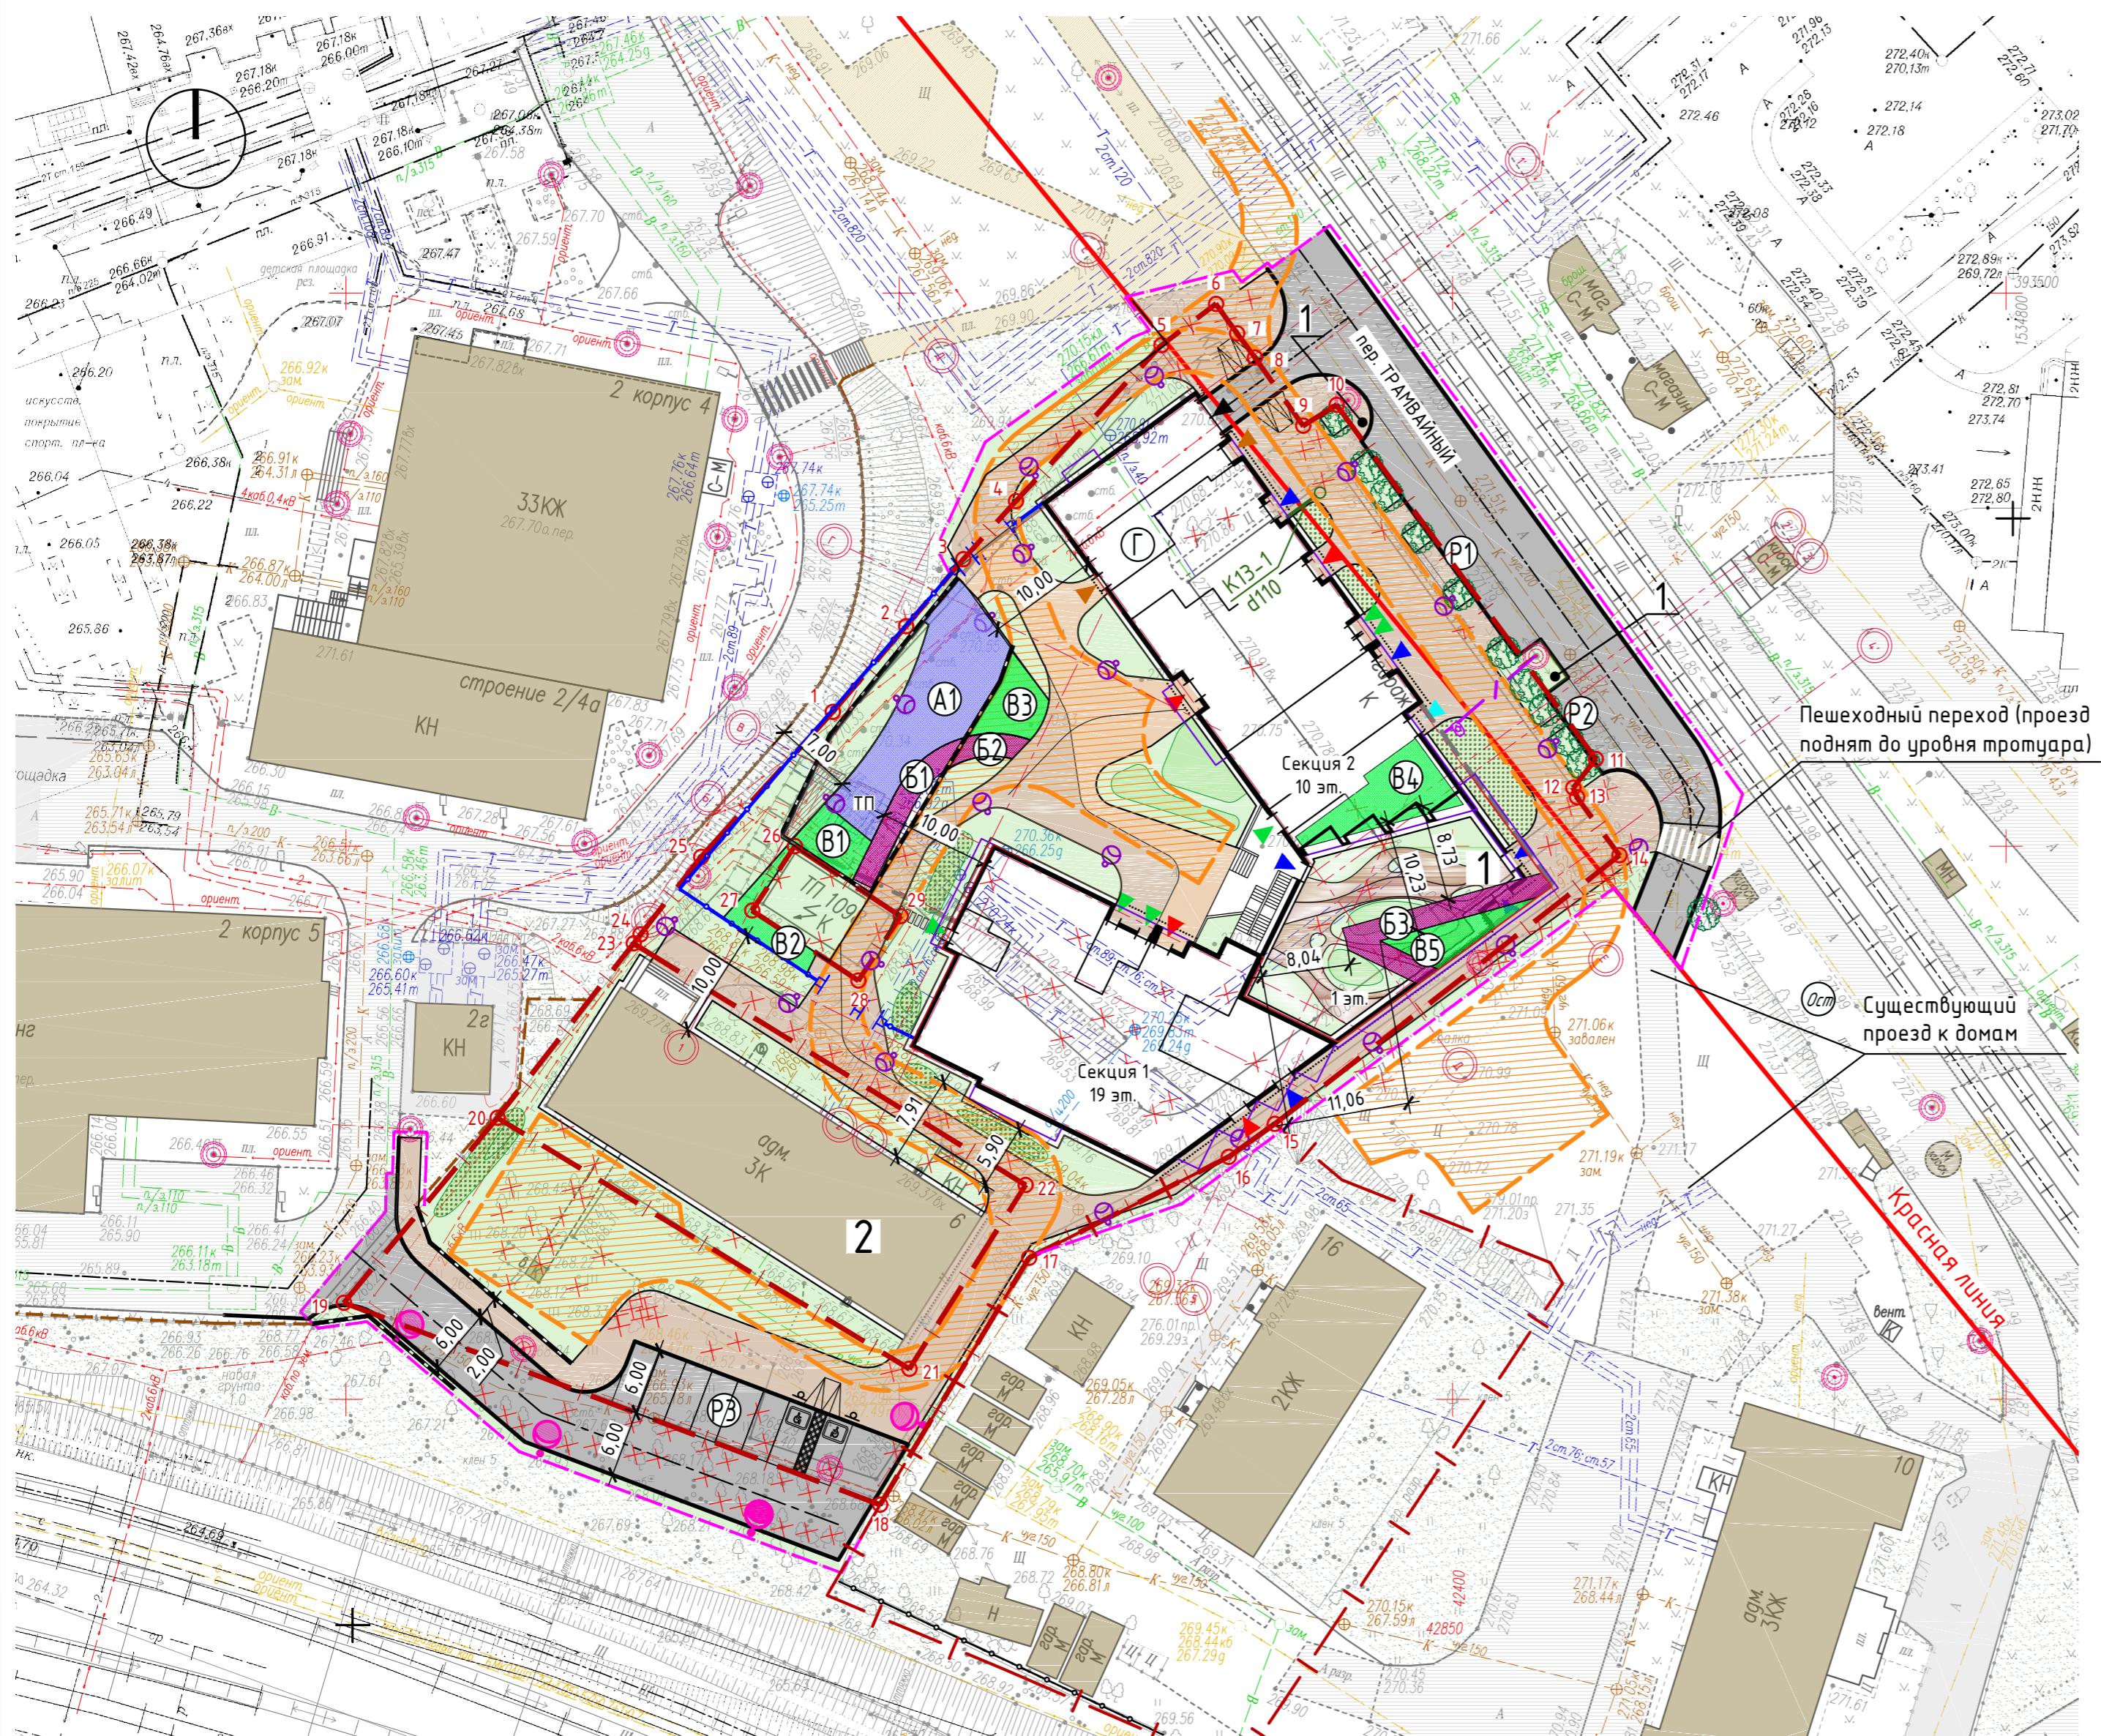

Условные графические обозначения

Инв. № участка
Лицензия на право
Влад. инф. N

- Красная линия
- Граница земельного участка (4 759 м²)
- Граница благоустройства (5 976 м²)
- Граница подземной автостоянки
- Граница навесающих частей здания
- Подпорная стена
- Ограждение с воротами и калиткой (проект.)
- Ограждение (сущ.)
- ▲ Вход в жилые помещения
- ▲ Вход в помещения коммерческого назначения
- ▲ Вход в разгрузочное помещение
- ▲ Вход в технические помещения
- ▲ Въезд в подземную автостоянку
- ▲ Вход в мусорокамеру
- Движение пешеходов на мусорную площадку
- 1-29 Поворотные точки границы землеотвода

- Асфальтобетонное покрытие проездов и тротуаров (сущ.)
- Асфальтобетонное покрытие проездов (проект.)
- Покрытие из бетонной плитки тротуаров (проект.)
- Озеленение/газон (проект.)
- Озеленение/газон (сущ.)
- Место размещения опоры освещения

- ▲ Место понижения бортового камня для ММГН (1,50 x 3,0 м)
- Место для стоянки легкового автомобиля, принадлежащего инвалиду-колясочнику.
- ||||| Существующий пешеходный переход
- Существующие деревья
- Существующие ограждения
- Дорожный знак 3.28 "Стоянка запрещена"

Номер по плану	Наименование	Примечание
Проектируемые здания и сооружения		
1	Многоквартирный жилой дом секционного типа со встроеннымными помещениями коммерческого назначения, с подземными техническими этажами (в т. ч. встроенной трансформаторной подстанцией) и подземным паркингом, в т.ч.:	
C1	19-этажная жилая секция со встроенно-пристроенными помещениями коммерческого назначения	
C2	10-этажная жилая секция со встроено-пристроенными помещениями коммерческого назначения	
Существующие здания и сооружения		
2	Административное здание	

Ведомость площадок

Числовое изображение или обозначение	Наименование	Примечание
(A1)	Площадка для игр детей 1	140 м ²
(B1)	Площадка для отдыха взрослых 1	29 м ²
(B2)	Площадка для отдыха взрослых 2	11 м ²
(B3)	Площадка для отдыха взрослых 3 (на кровле пристроя)	50 м ²
(B1)	Площадка для занятий физкультурой 1	28 м ²
(B2)	Площадка для занятий физкультурой 2	30 м ²
(B3)	Площадка для занятий физкультурой 3	32 м ²
(B4)	Площадка для занятий физкультурой 4 (на кровле секции C2)	53 м ²
(B5)	Площадка для занятий физкультурой 5 (на кровле пристроя)	31 м ²
(Г)	Встроенная мусорокамера	
(P1)	Парковочный карман для разгрузки/погрузки	проект.
(P2)	Парковочный карман для остановки такси	проект.
(P3)	Открытая автостоянка на 8 машино-мест	проект.
(Ост)	Остановка трамвая	сущ.

24-0104-20-ПЗУ

2	-	зам. 002-24	22.24	Жилой комплекс со встроено-пристроенными помещениями общественного назначения и подземной автостоянкой по адресу: пер. Трамвайный, д. 4, г. Екатеринбурга. Кадастровый номер участка 66:41:0205019:1881
1	-	зам. 001-24	10.24	
Изм.	Кол.ч.	Лист N док.	Форм. Дата	
Разраб.	Азаренкова	09.24		
Проверил	Шмидт	09.24		
ГИП	Шмидт	09.24		
Н.Контр				
Схема планировочной организации земельного участка. М 1:500				000 ПБ "АРМ"
Стадия	Лист	Листов		
П	2			